


-----

CORTES ESTRUCTURALES DE LOSA DE ENTREPISO PLANTA BAJA (TIPO)
SCALE: 1:100

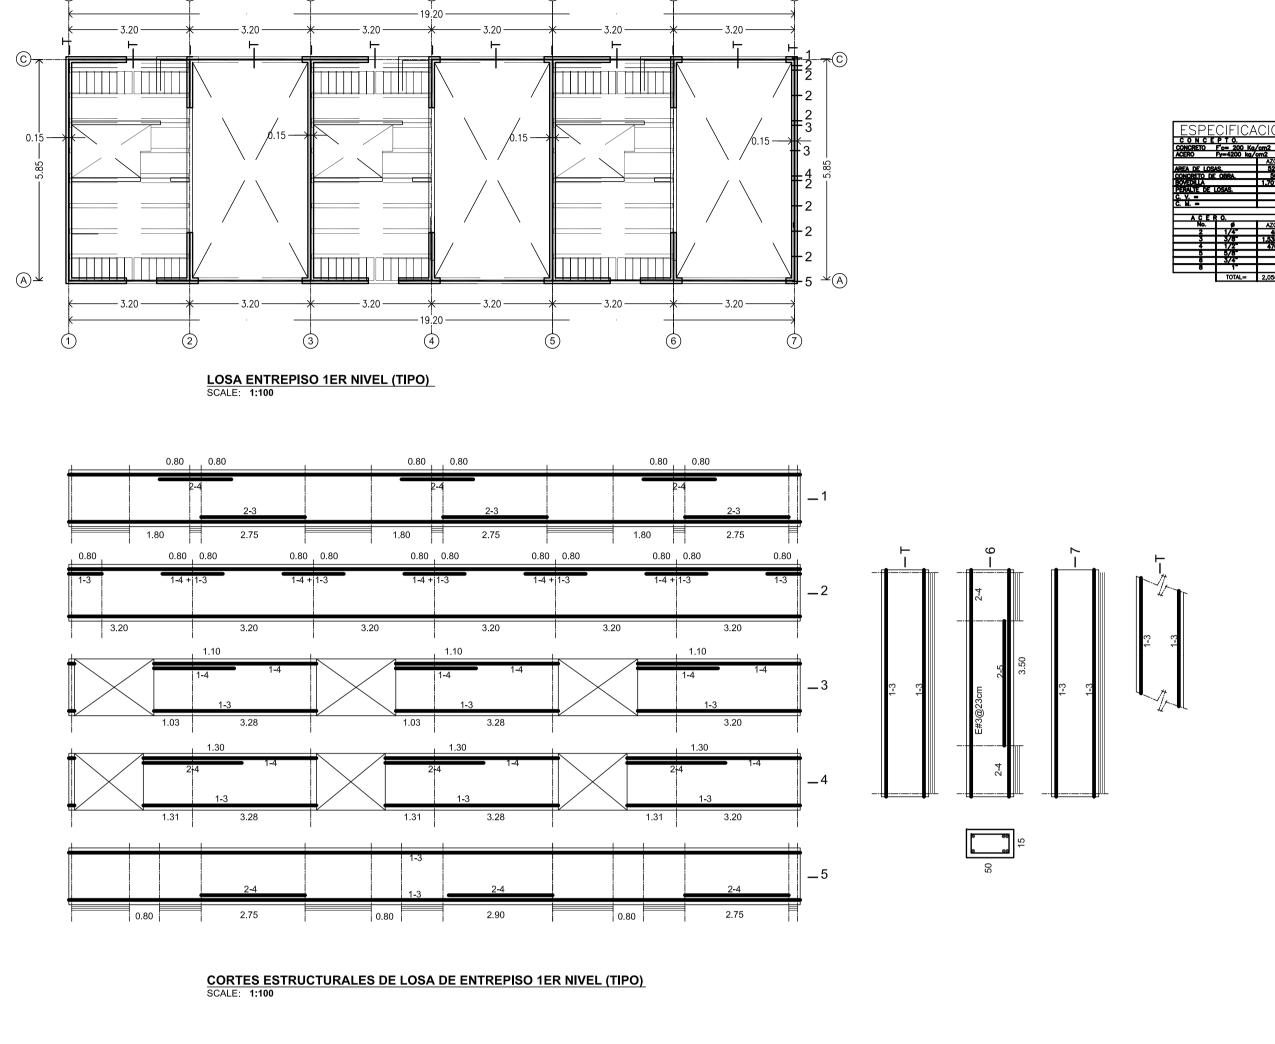

Wu= 688.0kg/m2 Wu= 461.0kg/m

ISOMETRIA DE PUNTALES

MALLA ELECTROSOLDADA 6-6/10-10


CASTILLO K-2
CMS. SIN/E
4 Vrs. # 3
Est. # 2
② 20.0 cms.

S/E

20 - 20 - VR # 4 @ 21 CM.

CORTE DE CIMENTACION A-A'

DETALLES DE CIMENTACION

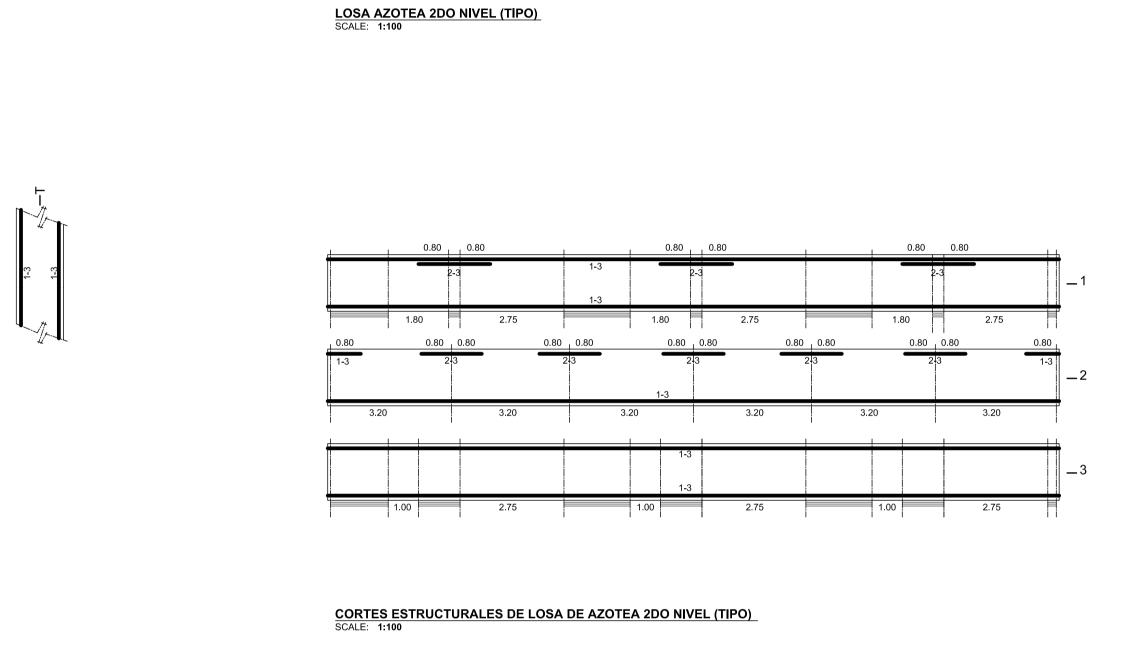

TEMPERATURA

ELEMENTAL MONTERREY

DIRECCION:

Av. Las Anacuas, Santa Catarina

MANDANTE:

Instituto de Vivienda de Nuevo León

ARQUITECTOS:

Alejandro Aravena M.
Fdo García-Huidobro

CONTENIDO:

PERMISO DE EDIFICAIÓN
DETALLES

EMITIDO PARA:

--
ARCHIVO:
ELEMENTAL-MONTERREY-DET.dwg

ELEMENTAL PROYECTO:

FECHA: 08/05/08 ESCALA: 1:75 REV: A TAMAÑO: A1 EXT.

A 08/05/08 DC XX